

PT. PRANSORPORA merupakan perusahaan pengembang real estate yang berada di Balikpapan. Perusahaan ini berdiri pada tahun 2012.

Perusahaan kami telah mengambil alih beberapa pengembang properti di kawasan Balikpapan yang memiliki masalah keuangan. secara keseluruhan, PRANSCORPORA sedang mengembangkan lahan seluas 50 hektar untuk hunian dan kawasan industri.

Menjadi perusahaan properti yang proaktif dan inovatif dengan tujuan untuk meningkatkan kehidupan yang memenuhi syarat bagi penduduk dan melestarikan lingkungan alam; menjadi perusahaan multinasional yang menguntungkan dengan tingkat pengembalian yang lebih baik bagi investor dan masyarakat; dan menjadi inspirator untuk menumbuhkan semangat kewirausahaan bangsa kita untuk memperkuat profil kita sebagai perusahaan yang bertanggung jawab secara sosial.

Portofolio

1. Rumah Type Palm A



SHOP DRAWING
RUMAH TYPE PALM - A
LUAS BANGUNAN = 77 m²


SPESIFIKASI TEKNIK :

- PONDASI	: TAPAK BETON BERTULANG
- DINDING	: PAS. BATU BATA PLESTER ACIAN
- LANTAI	: KERAMIK 40/40 CM & 30/30 CM
- SANITAIR	: KLOSET DUDUK EX. TOTO
- RANGKA ATAP	: BAJA RINGAN , GENTENG METAL FLAT
- KUSEN	: ALUMINIUM DAUN LAPIS PINTU HPL
- PLAFOND	: GYPSUM RANGKA HOLLOW
- SUMBER AIR	: PDAM
- LISTRIK	: PLN DAYA 2200 VA


PT. KISINDO INTI RAYA
Real Estate, Mining, And Heavy Equipment
Sentra Eropa 3 Blok AC I No. 1, Bollipapan Baru, Kal-Tim
Telepon : 0542-7127777, 0542-7167777
Email : kisindointiraya@yahoo.com

RUMAH TYPE PALM-A
PERUMAHAN BUKIT VILLA
KOTA BALIKPAPAN, KALTIM

JUDUL GAMBAR	SKALA	NO. GAMBAR
GAMBAR DETAIL		

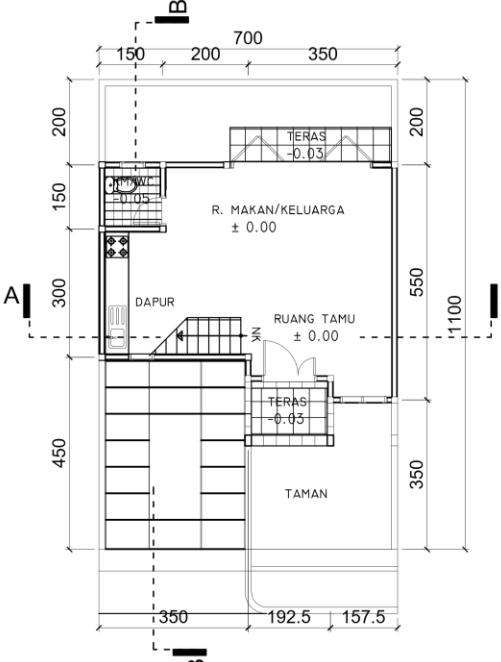

DENAH LANTAI BAWAH
SKALA 1:100


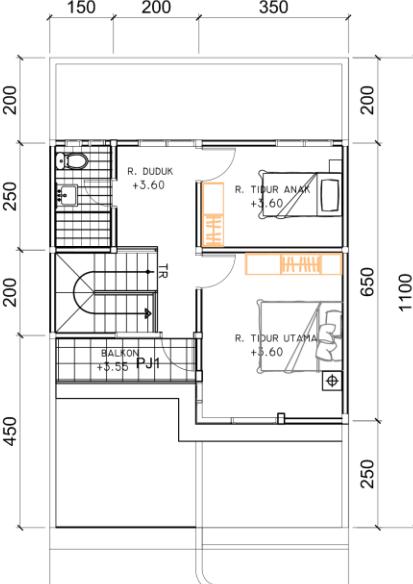




DENAH LANTAI ATAS
SKALA 1:100



PT. KISINDO INTI RAYA
Real Estate, Mining, And Heavy Equipment
Sentra Eropa 3 Blok AC I No. 1, Bollipapan Baru, Kal-Tim
Telepon : 0542-7127777, 0542-7167777
Email : kisindointiraya@yahoo.com



RUMAH TYPE PALM A
PERUMAHAN BUKIT VILLA
KOTA BALIKPAPAN, KALTIM

JUDUL GAMBAR	SKALA	NO. GAMBAR
• DENAH LT. BAWAH	1:100	
• DENAH LT. ATAS	1:100	
GAMBAR DETAIL		

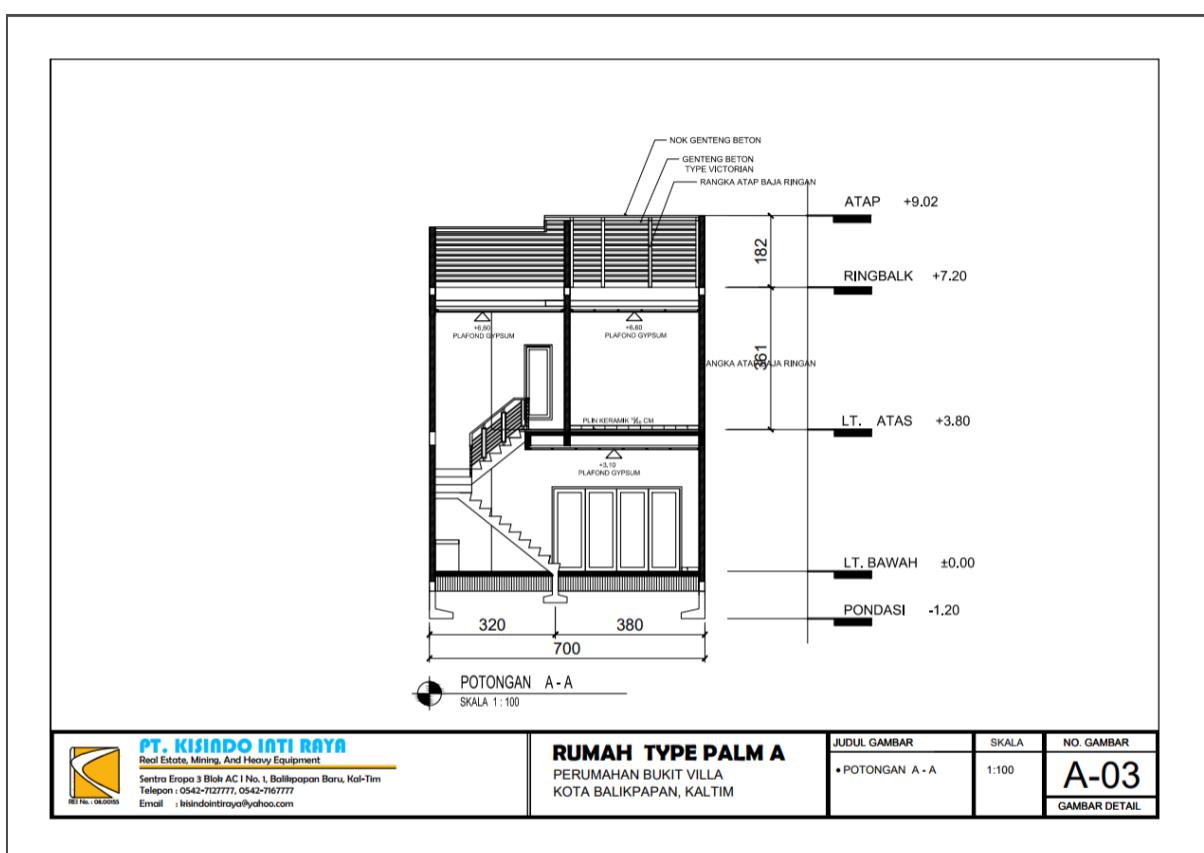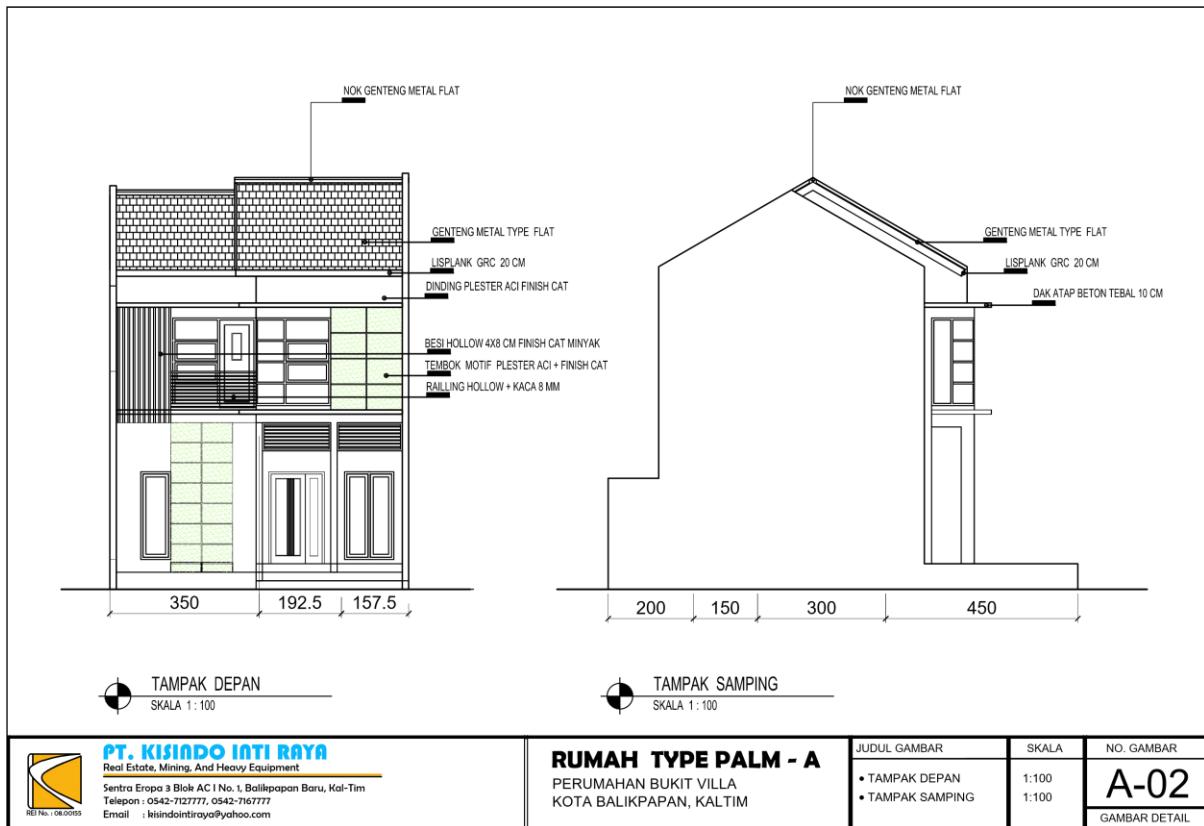

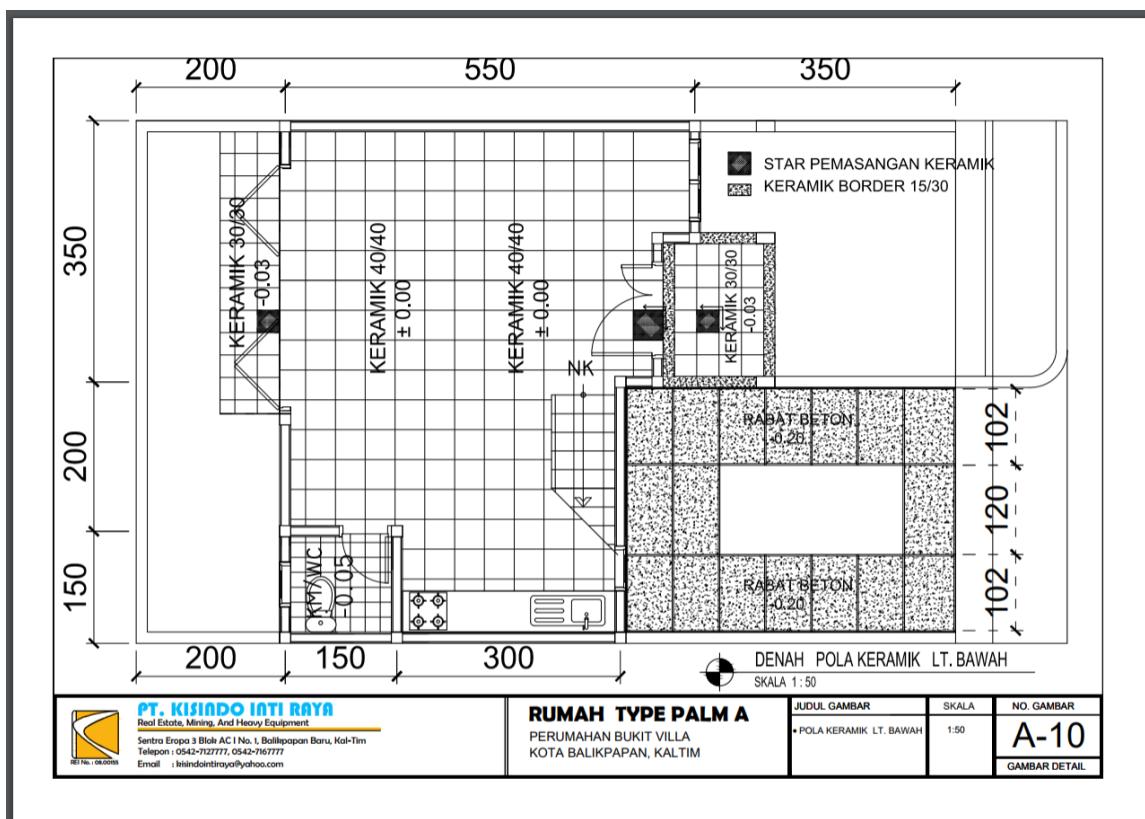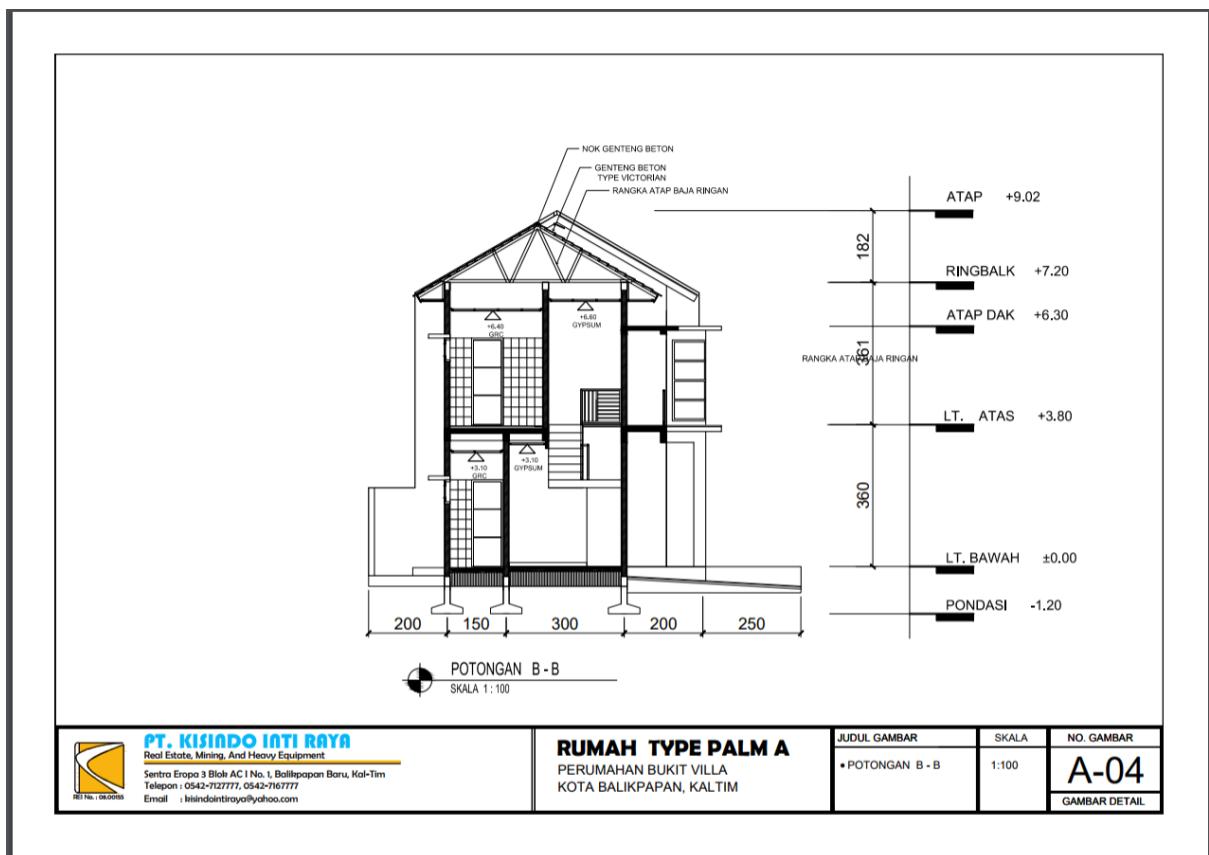

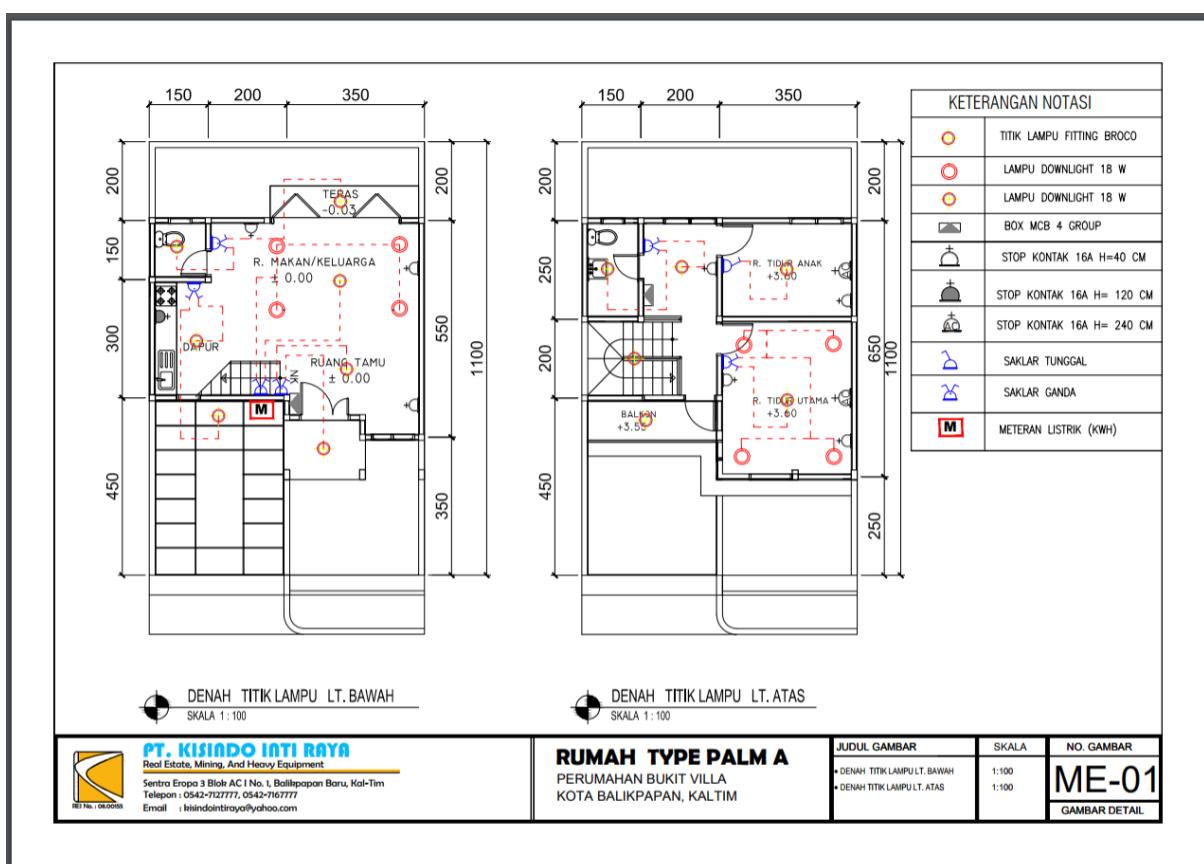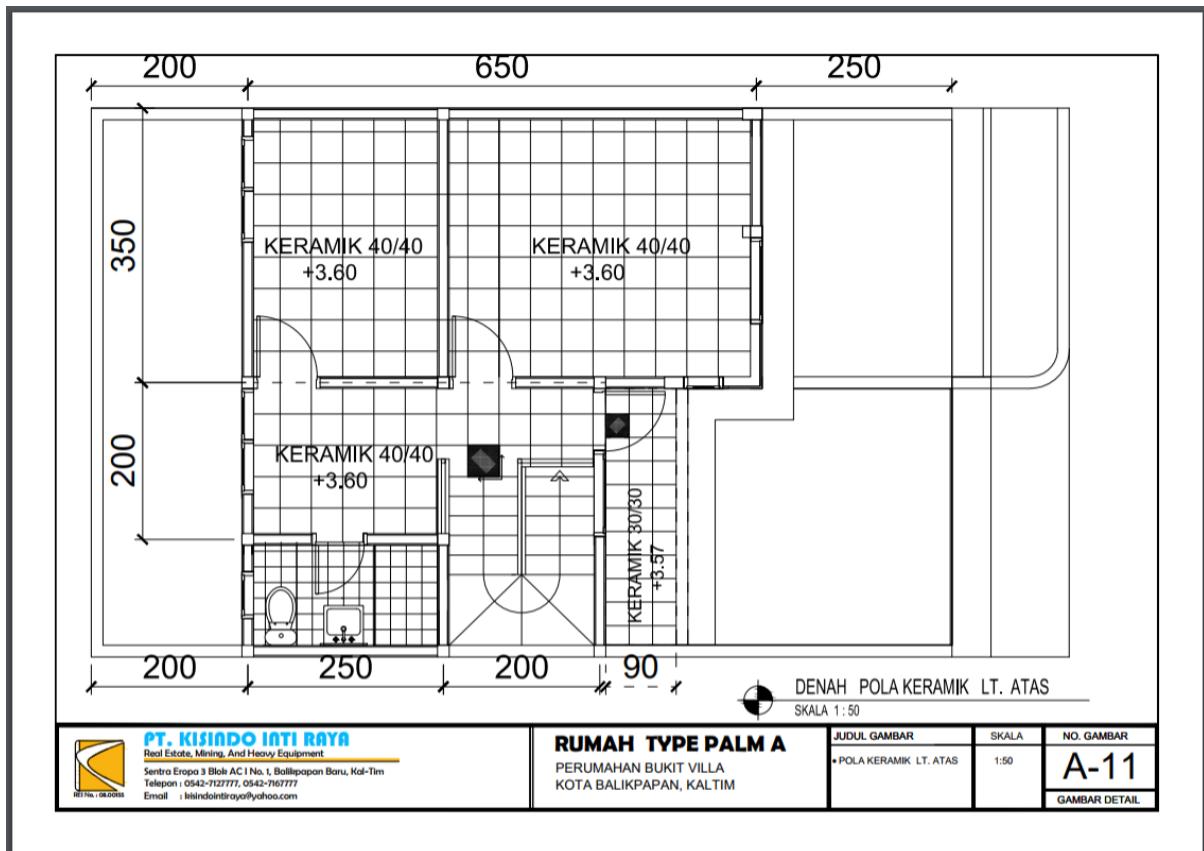

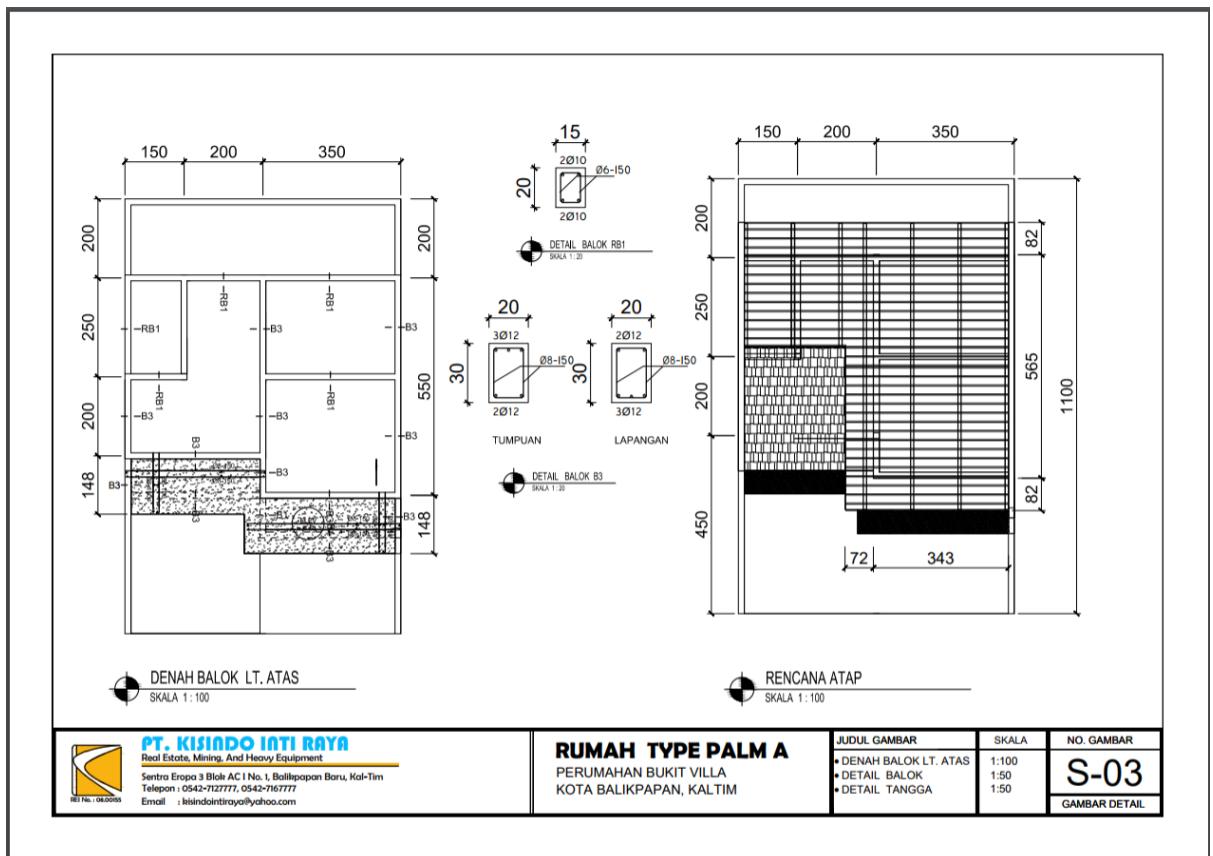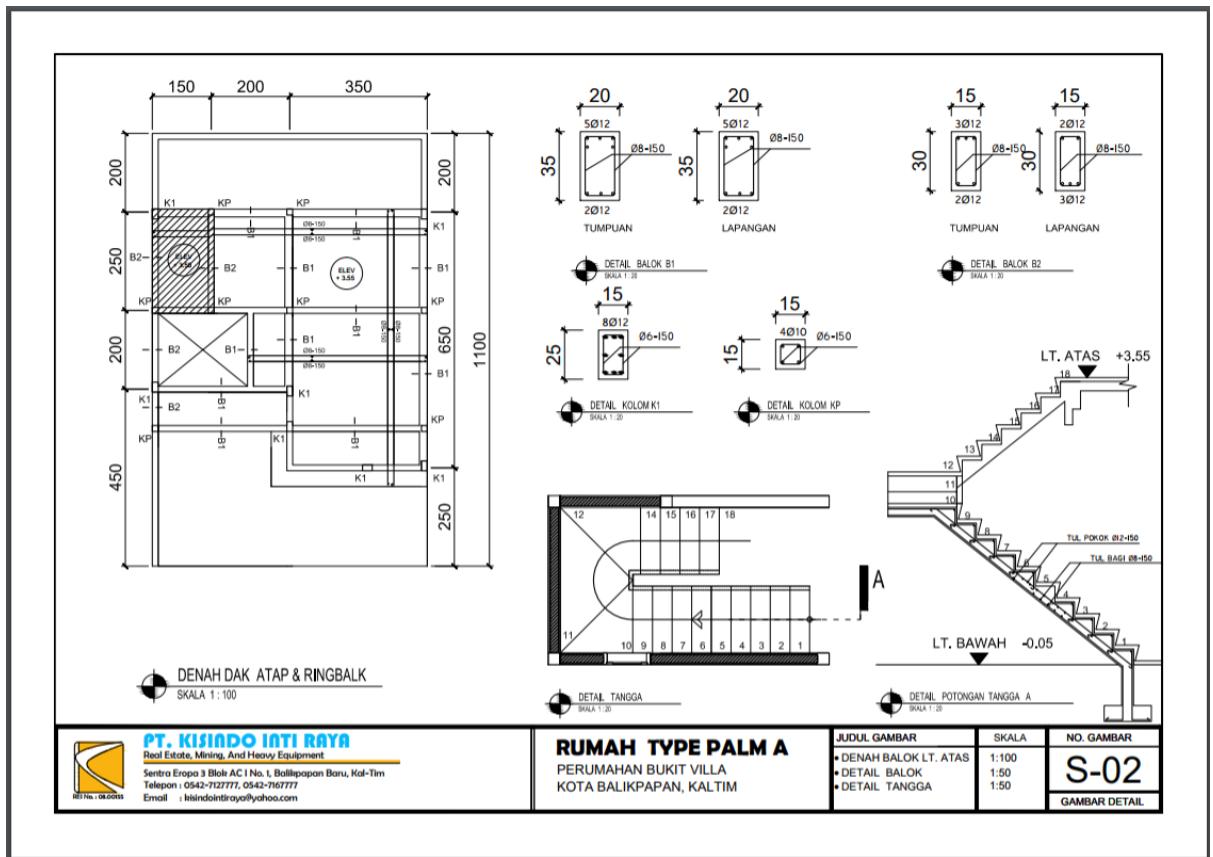

2. Rumah Type Palm B



SHOP DRAWING
RUMAH TYPE PALM - B
LUAS BANGUNAN = 77 m²


SPECIFIKASI TEKNIK :

- PONDASI	: TAPAK BETON BERTULANG
- DINDING	: PAS, BATU BATA PLESTER ACIAN
- LANTAI	: KERAMIK 40/40 CM & 30/30 CM
- SANITAIR	: KLOSET DUDUK EX. TOTO
- RANGKA ATAP	: BAJA RINGAN, GENTENG METAL FLAT
- KUSEN	: ALUMINUM DAUN LAPIS PINTU HPL
- PLAFOND	: GYPSUM RANGKA HOLLOW
- SUMBER AIR	: PDAM
- LISTRIK	: PLN DAYA 2200 VA


PT. KISINDO INTI RAYA
Real Estate, Mining, And Heavy Equipment
Senter Eropa 3 Blok AC I No. 1, Balikpapan Baru, Kal-Tim
Telepon : 0542-7127777, 0542-7167777
Email : kisindointiraya@yahoo.com

RUMAH TYPE PALM-B
PERUMAHAN BUKIT VILLA
KOTA BALIKPAPAN, KALTIM

JUDUL GAMBAR	SKALA	NO. GAMBAR
GAMBAR DETAIL		

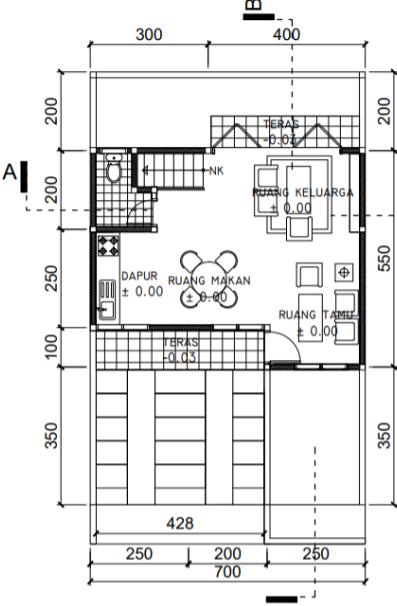

DENAH LANTAI BAWAH
SKALA 1:100

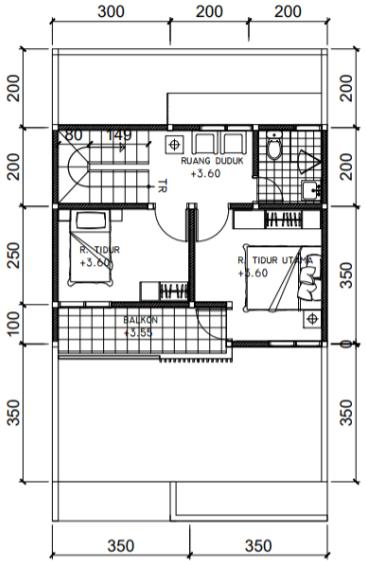



DENAH LANTAI ATAS
SKALA 1:100



PT. KISINDO INTI RAYA
Real Estate, Mining, And Heavy Equipment
Senter Eropa 3 Blok AC I No. 1, Balikpapan Baru, Kal-Tim
Telepon : 0542-7127777, 0542-7167777
Email : kisindointiraya@yahoo.com


RUMAH TYPE PALM B
PERUMAHAN BUKIT VILLA
KOTA BALIKPAPAN, KALTIM

JUDUL GAMBAR	SKALA	NO. GAMBAR
• DENAH LT. BAWAH	1:100	
• DENAH LT. ATAS	1:100	
GAMBAR DETAIL		


A-01

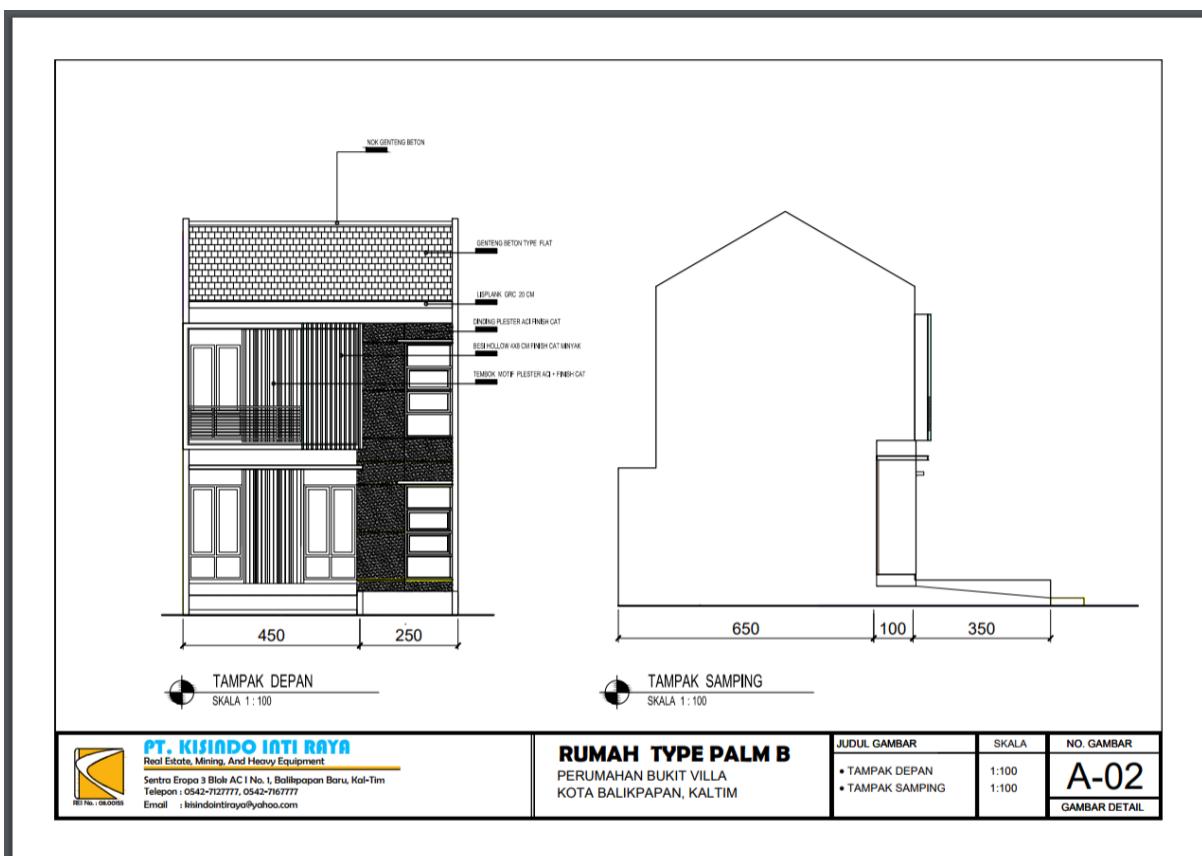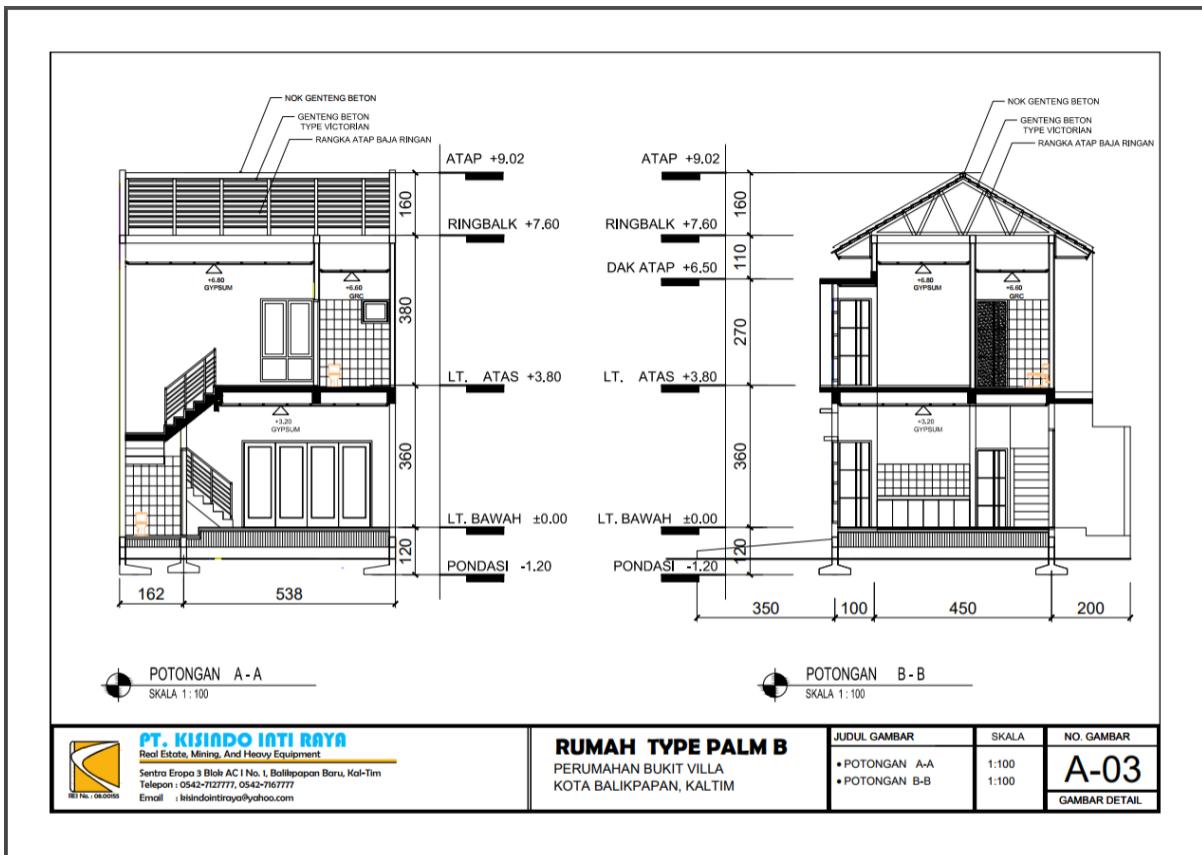

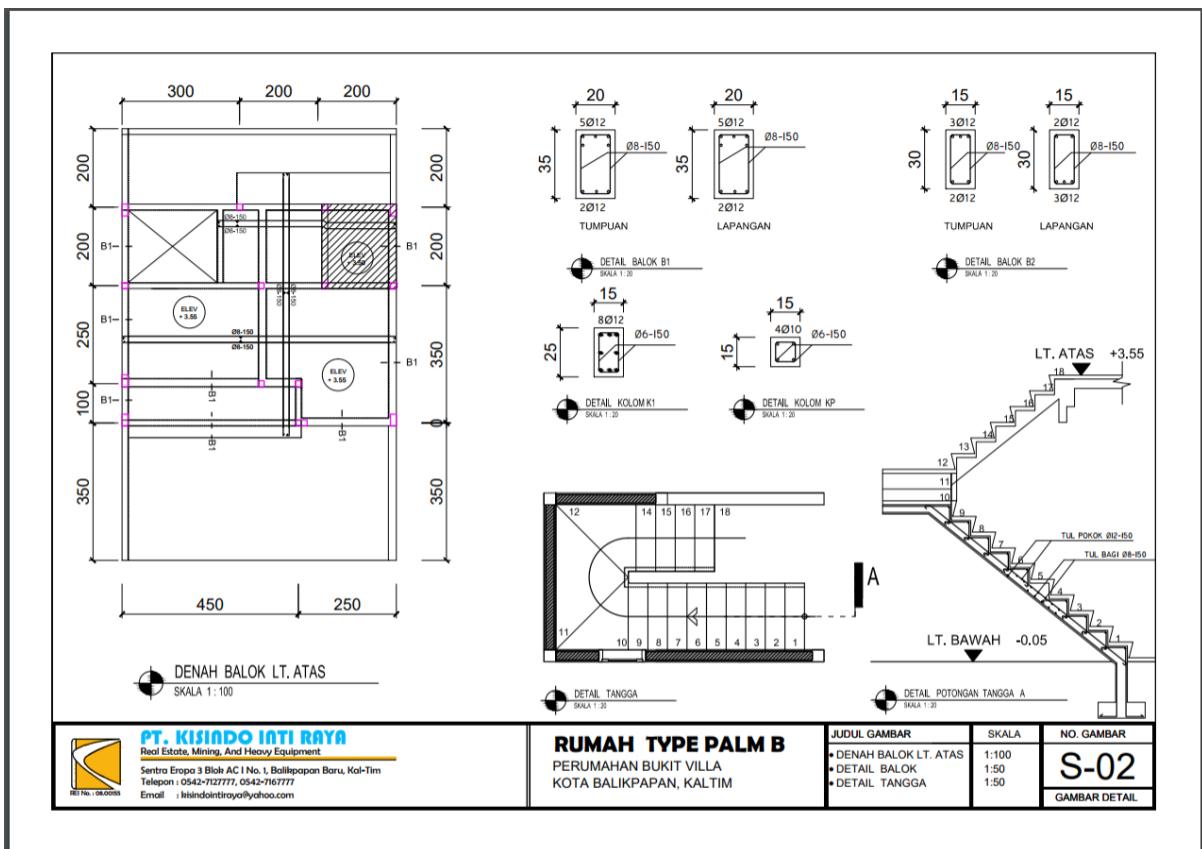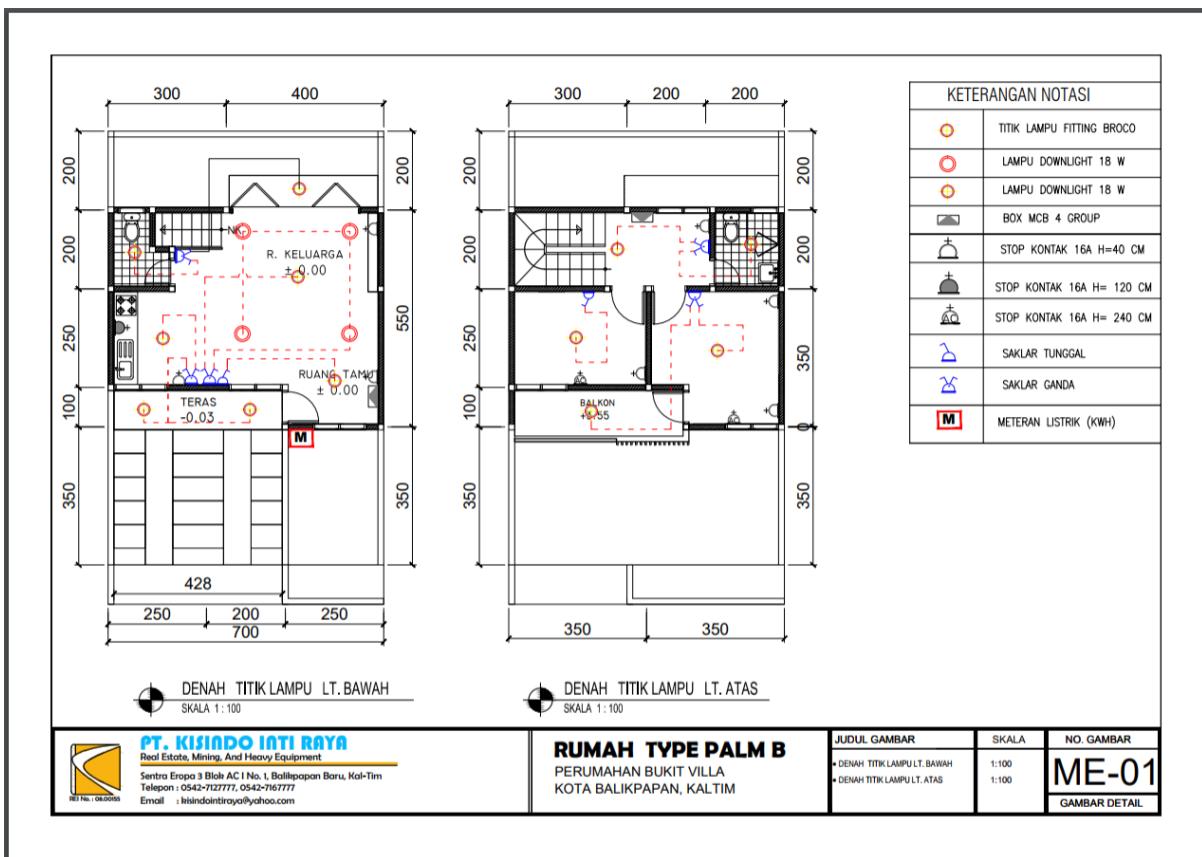


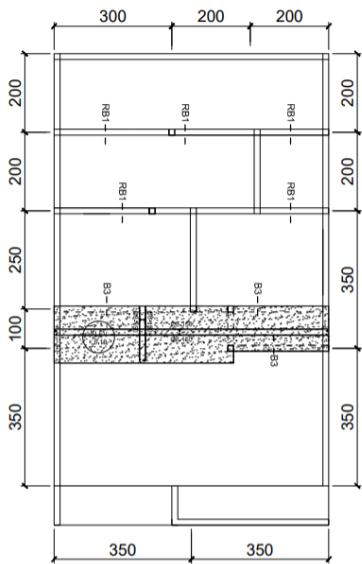

DENAH DAK ATAP & RINGBALK
SKALA 1:100

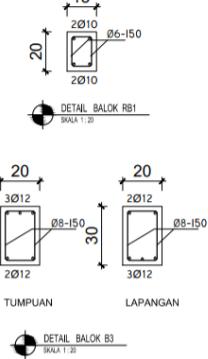

RENCANA ATAP
SKALA 1:100

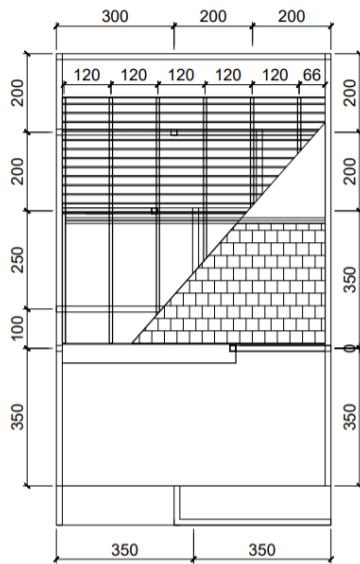

PT. KISINDO INTI RAYA
Real Estate, Mining, And Heavy Equipment
Sentra Eropa 3 Blok AC I No. 1, Bontang Baru, Kalimantan Timur
Telepon : 0542-7127777, 0542-7167777
Email : kisindointiraya@yahoo.com

RUMAH TYPE PALM B

PERUMAHAN BUKIT VILLA
KOTA BALIKPAPAN, KALTIM

JUDUL GAMBAR	SKALA	NO. GAMBAR
• DENAH DAK ATAP DAN RING BALK	1:100	
• DETAIL BALOK & RINGBALK • RENCANA ATAP	1: 20 1:100	S-03 GAMBAR DETAIL

3. Rumah Type Palm C



SHOP DRAWING

RUMAH TYPE PALM - C

LUAS BANGUNAN = 93 m²


SPESIFIKASI TEKNIK :

- PONDASI : TAPAK BETON BERTULANG
- DINDING : PAS. BATU BATA PLESTER ACIAN
- LANTAI : KERAMIK 40/40 CM & 30/30 CM
- SANITAIR : KLOSET DUDUK EX. TOTO
- RANGKA ATAP : BAJA RINGAN , GENTENG METAL FLAT
- KUSEN : ALUMINUM DAUN LAPIS PINTU HPL
- PLAFOND : GYPSUM RANGKA HOLLOW
- SUMBER AIR : PDAM
- LISTRIK : PLN DAYA 2200 VA

PT. KISINDO INTI RAYA
Real Estate, Mining, And Heavy Equipment
Sentra Eropa 3 Blok AC 1 No. 1, Balikpapan Baru, Kalimantan Timur
Telepon : 0542-7127777, 0542-7167777
Email : kisindointiraya@yahoo.com

RUMAH TYPE PALM - C
PERUMAHAN BUKIT VILLA
KOTA BALIKPAPAN, KALTIM

JUDUL GAMBAR	SKALA	NO. GAMBAR
		GAMBAR DETAIL

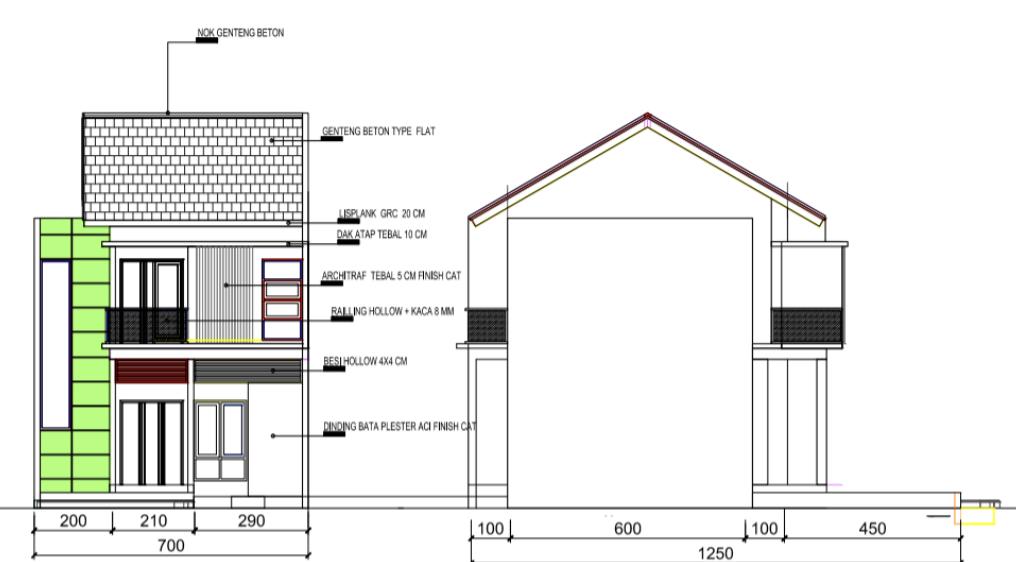



TAMPAK DEPAN SKALA 1:100



TAMPAK SAMPING SKALA 1:100


PT. KISINDO INTI RAYA
Real Estate, Mining, And Heavy Equipment
Sentra Eropa 3 Blok AC 1 No. 1, Balikpapan Baru, Kalimantan Timur
Telepon : 0542-7127777, 0542-7167777
Email : kisindointiraya@yahoo.com

RUMAH TYPE PALM - C
PERUMAHAN BUKIT VILLA
KOTA BALIKPAPAN, KALTIM



JUDUL GAMBAR	SKALA	NO. GAMBAR
• TAMPAK DEPAN	1:100	A-02
• TAMPAK SAMPING	1:100	
		GAMBAR DETAIL

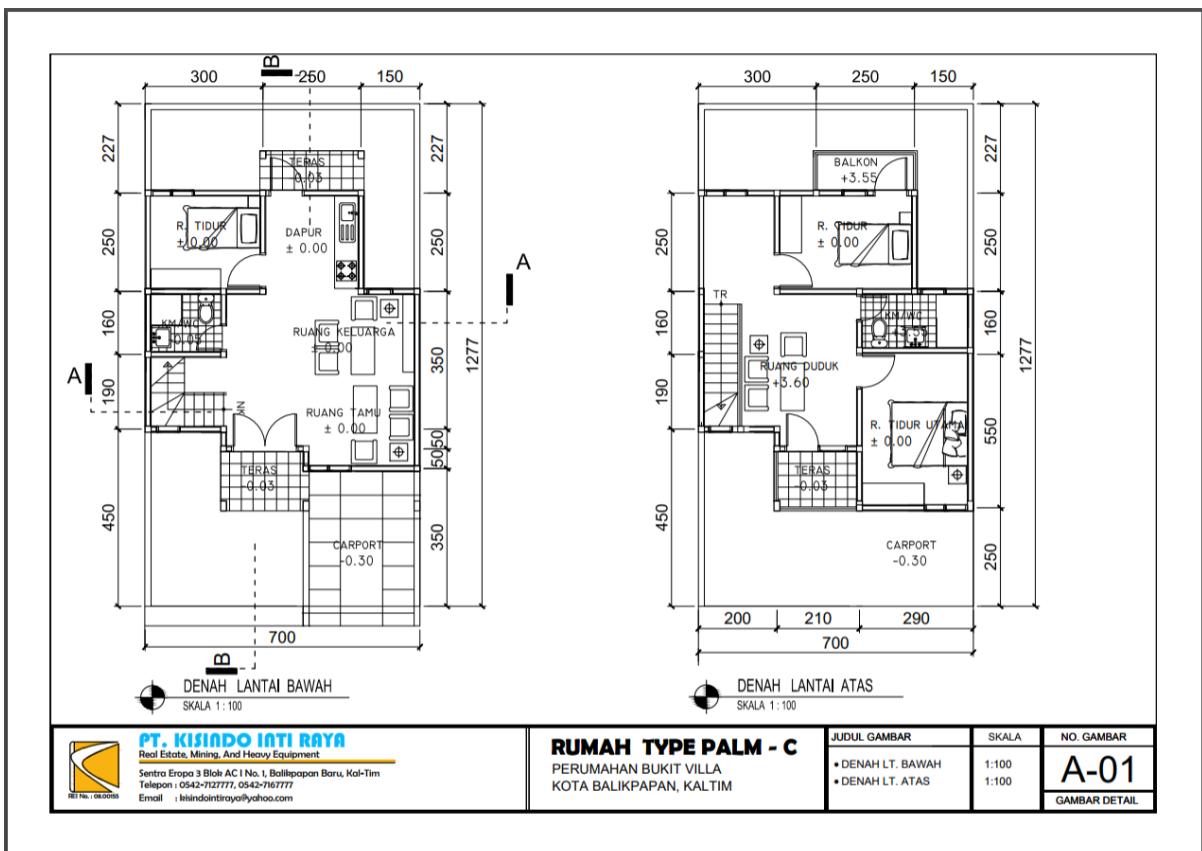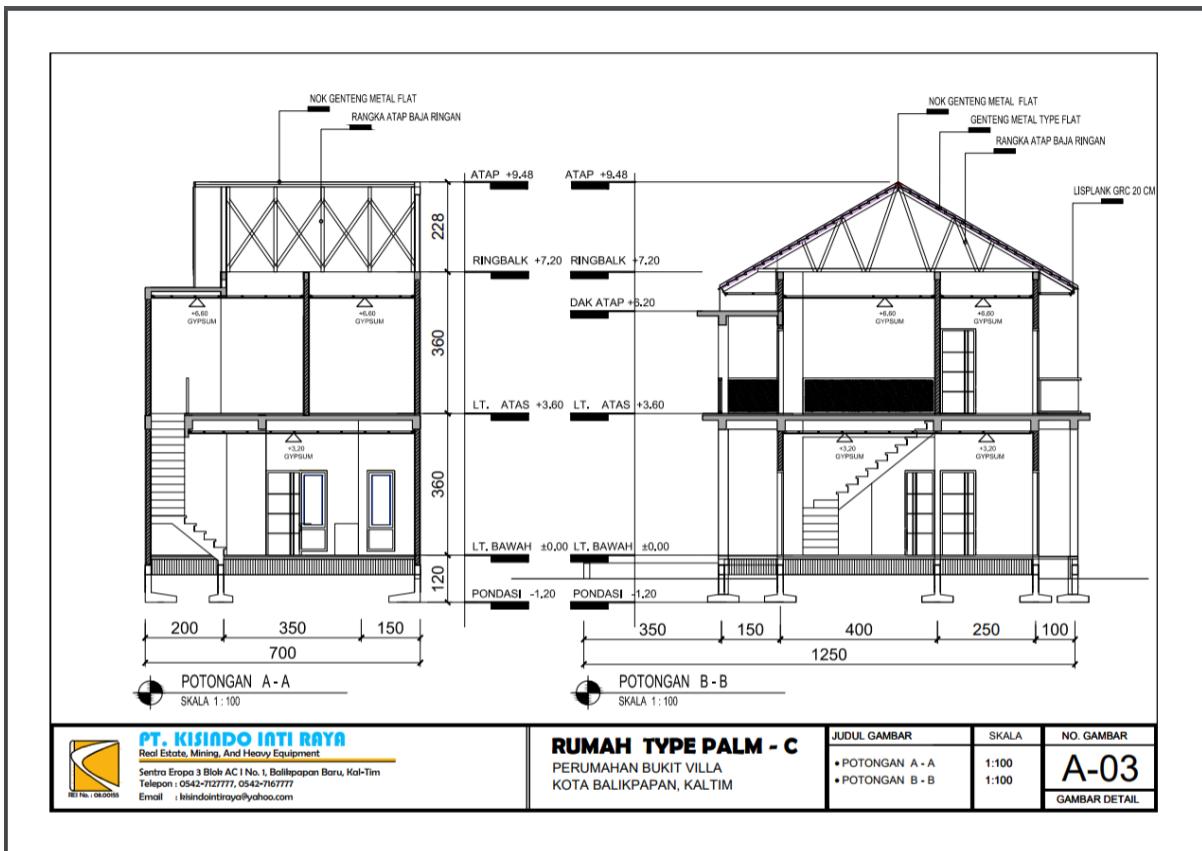

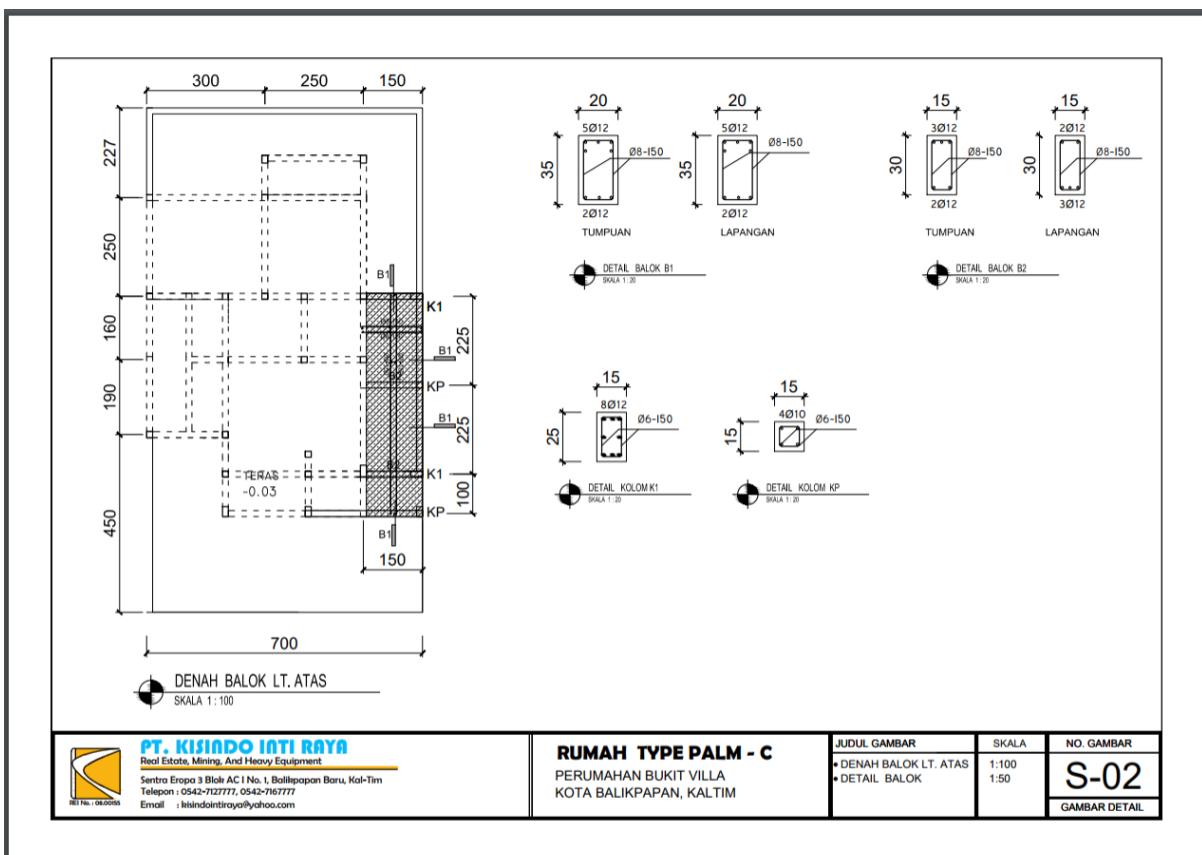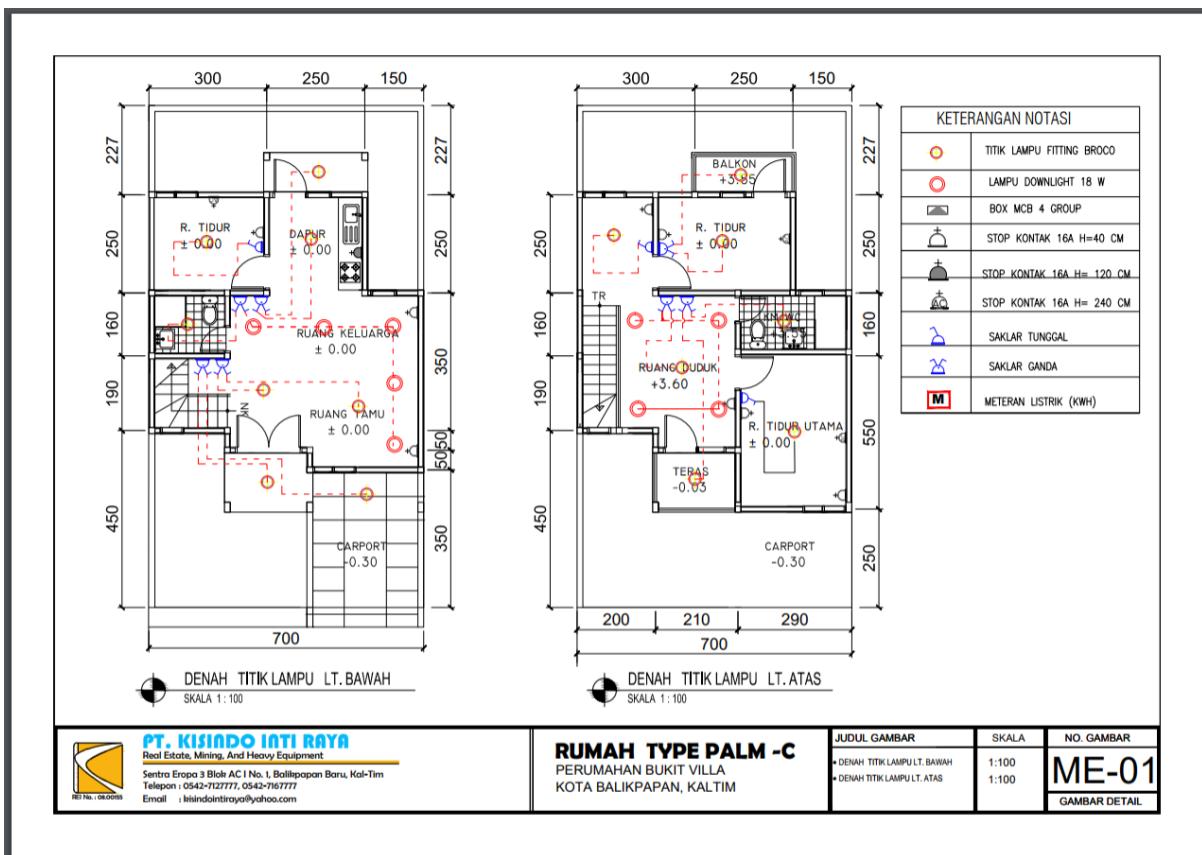

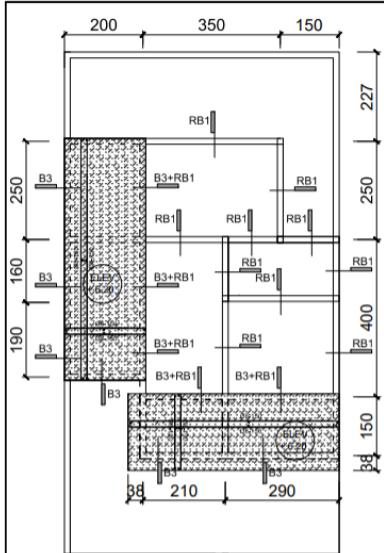

DENAH DAK ATAP & RINGBALK
SKALA 1:100

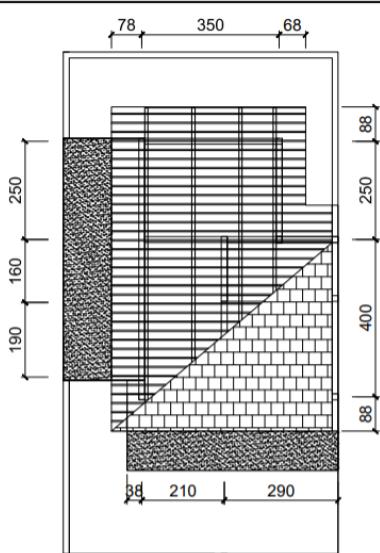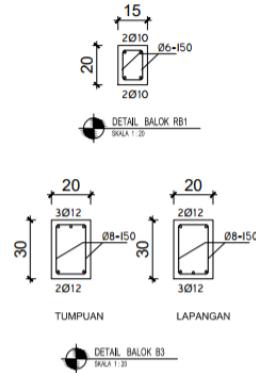

RENCANA ATAP
SKALA 1:100



PT. KISINDO INTI RAYA

Real Estate, Mining, And Heavy Equipment

Sentro Express 3 Blok A1 No. 1, Bontangpapan Baru, Kalimantan Timur
Telepon : 0542-7127777, 0542-7107777
Email : Kisindointiraya@yahoo.com

RUMAH TYPE PALM -C

PERUMAHAN BUKIT VILLA
KOTA BALIKPAPAN, KALTIM

JUDUL GAMBAR	SKALA	NO. GAMBAR
• DENAH DAK ATAP DAN RING BALK	1:100	S-03
• DETAIL BALOK & RINGBALK	1: 20	
• RENCANA ATAP	1:100	

GAMBAR DETAIL

4. Rumah Type Palm Sudut

SHOP DRAWING

RUMAH TYPE PALM SUDUT



LUAS BANGUNAN = 93 m²







SPECIFIKASI TEKNIK :


- PONDASI	: TAPAK BETON BERTULANG
- DINDING	: PAS. BATU BATA PLESTER ACIAN
- LANTAI	: KERAMIK 40/40 CM & 30/30 CM
- SANITAIR	: KLOSET DUDUK EX. TOTO
- RANGKA ATAP	: BAJA RINGAN , GENTENG METAL FLAT
- KUSEN	: ALUMINIUM DAUN LAPIS PINTU HPL
- PLAFOND	: GYPSUM RANGKA HOLLOW
- SUMBER AIR	: PDAM
- LISTRIK	: PLN DAYA 2200 VA

<p>PT. KISINDO INTI RAYA Real Estate, Mining, And Heavy Equipment Sentro Eropa 3 Blok AC I No. 1, Balikpapan Baru, Kal-Tim Telepon : 0542-7127777, 0542-7167777 Email : kisindointiraya@yahoo.com</p>	<p>RUMAH TYPE PALM SUDUT PERUMAHAN BUKIT VILLA KOTA BALIKPAPAN, KALTIM</p>	<table border="1" style="width: 100%;"><thead><tr><th>JUDUL GAMBAR</th><th>SKALA</th><th>NO. GAMBAR</th></tr></thead><tbody><tr><td> </td><td> </td><td> </td></tr><tr><td colspan="3">GAMBAR DETAIL</td></tr></tbody></table>	JUDUL GAMBAR	SKALA	NO. GAMBAR				GAMBAR DETAIL		
JUDUL GAMBAR	SKALA	NO. GAMBAR									
GAMBAR DETAIL											

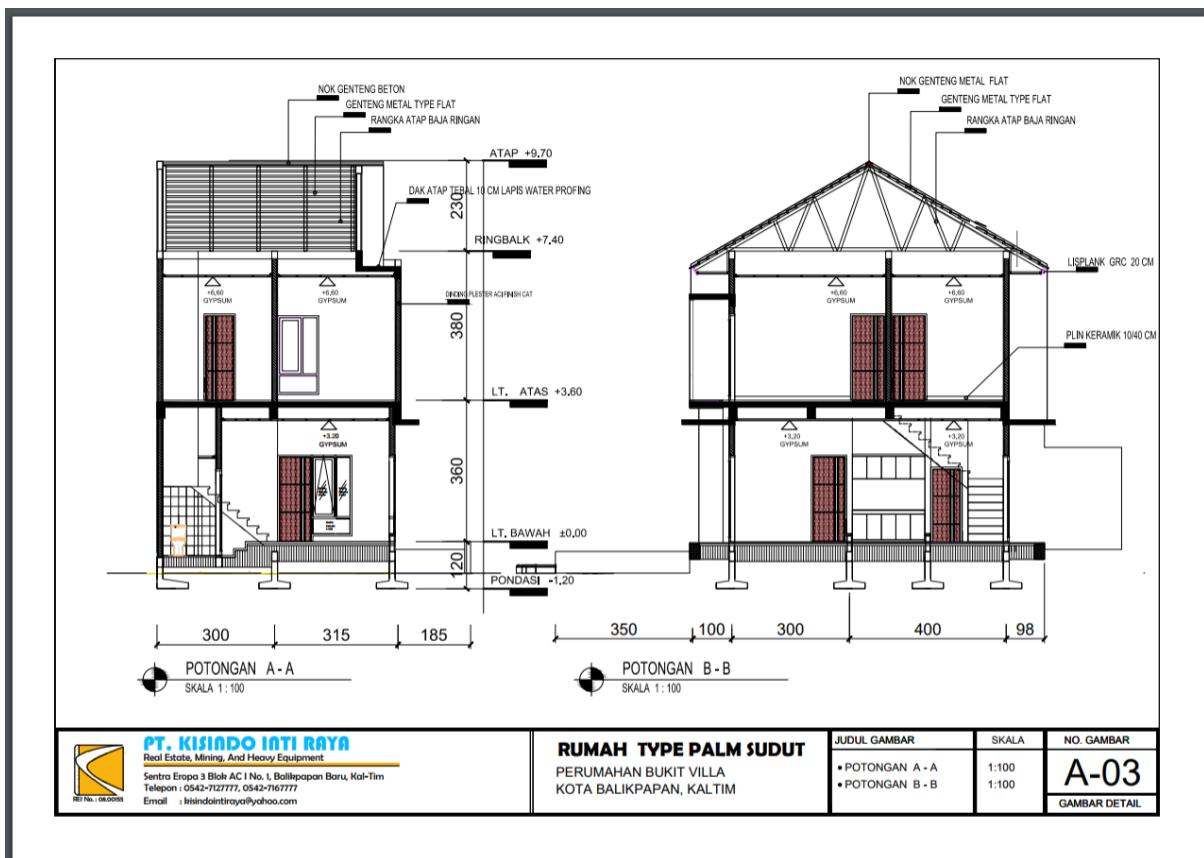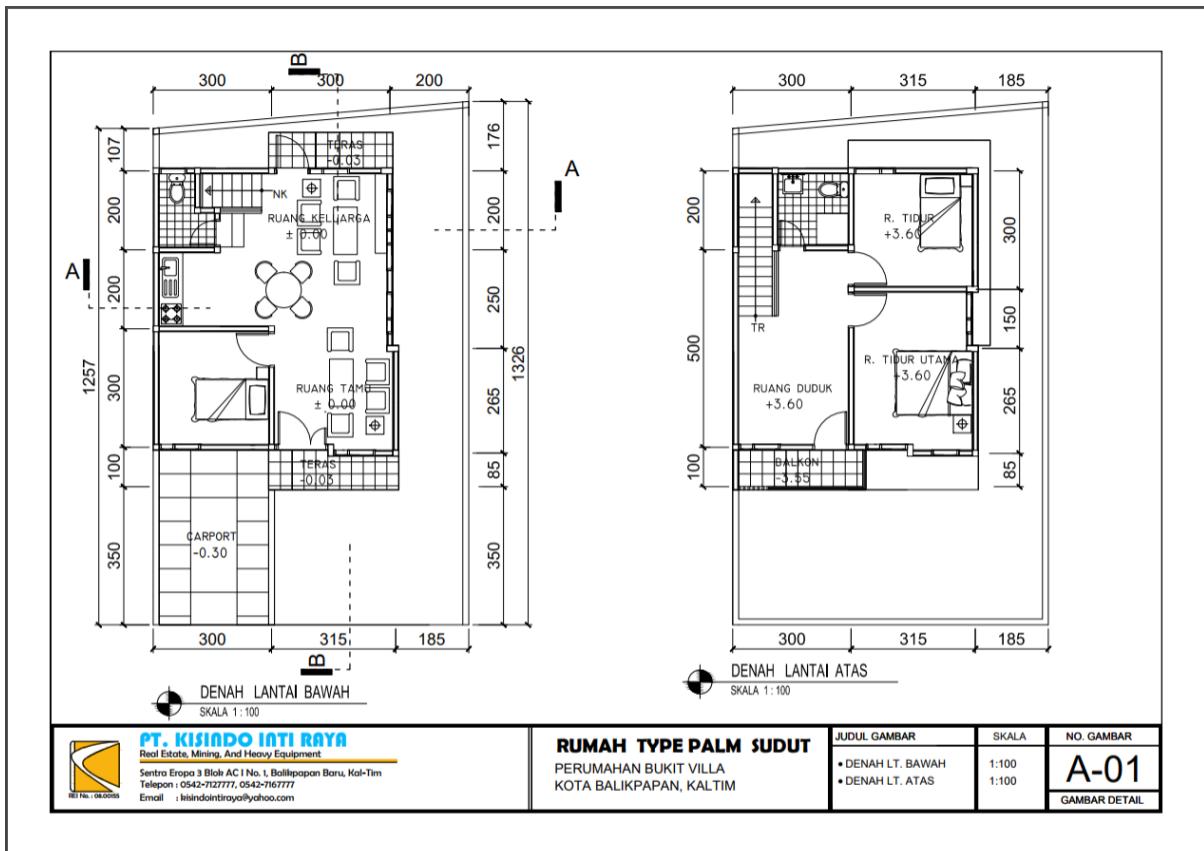

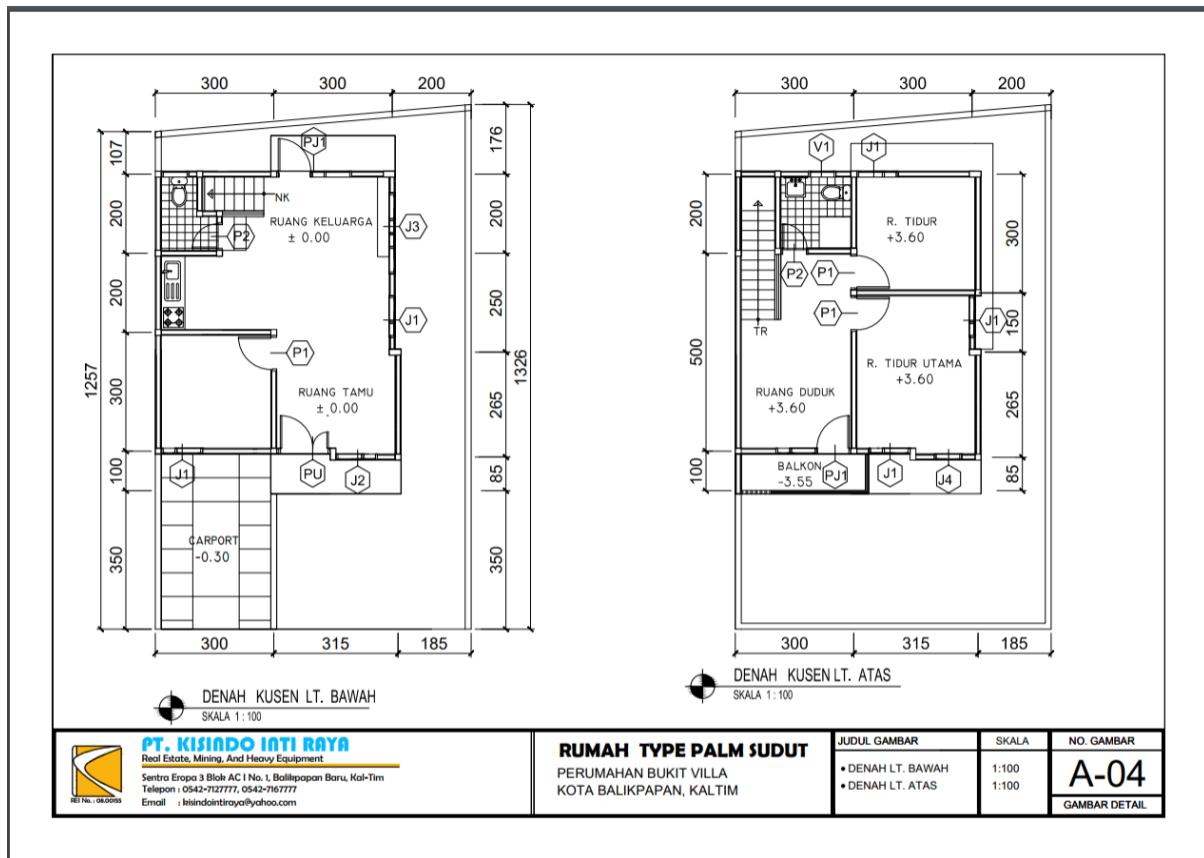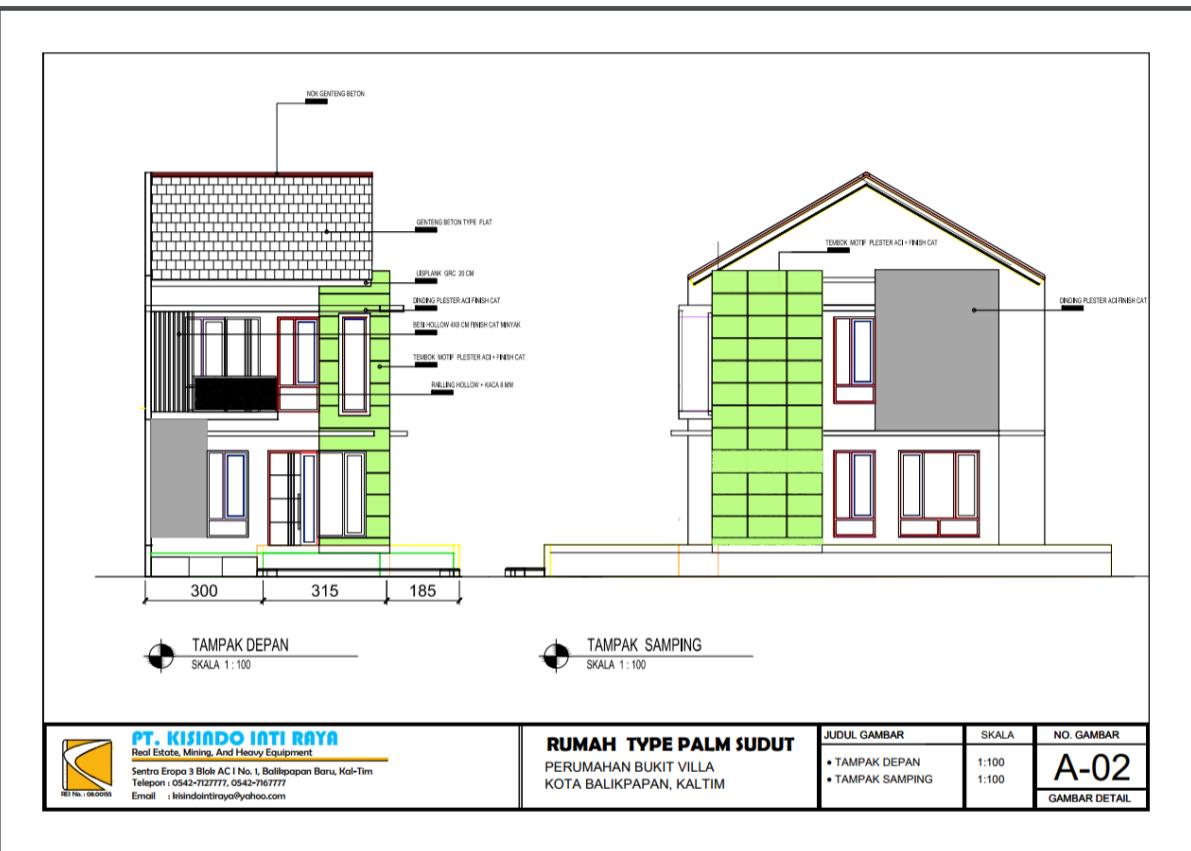

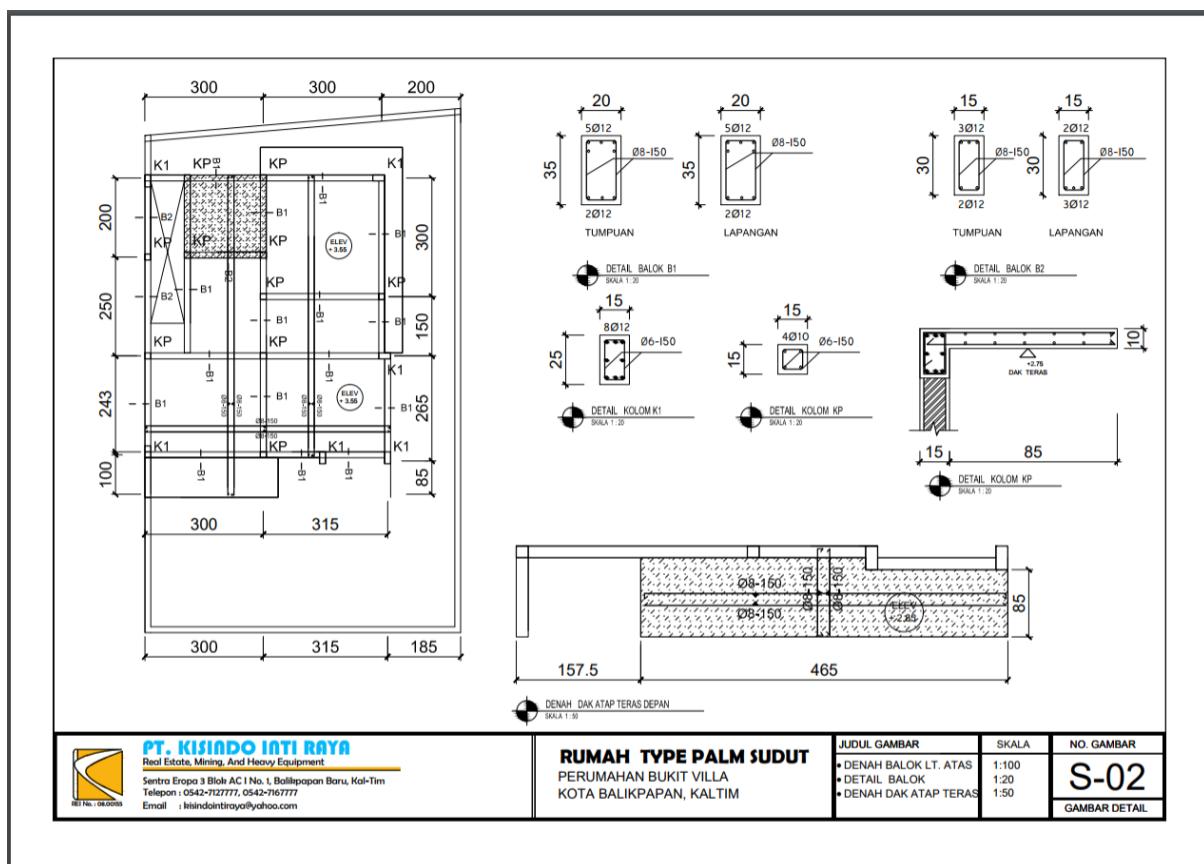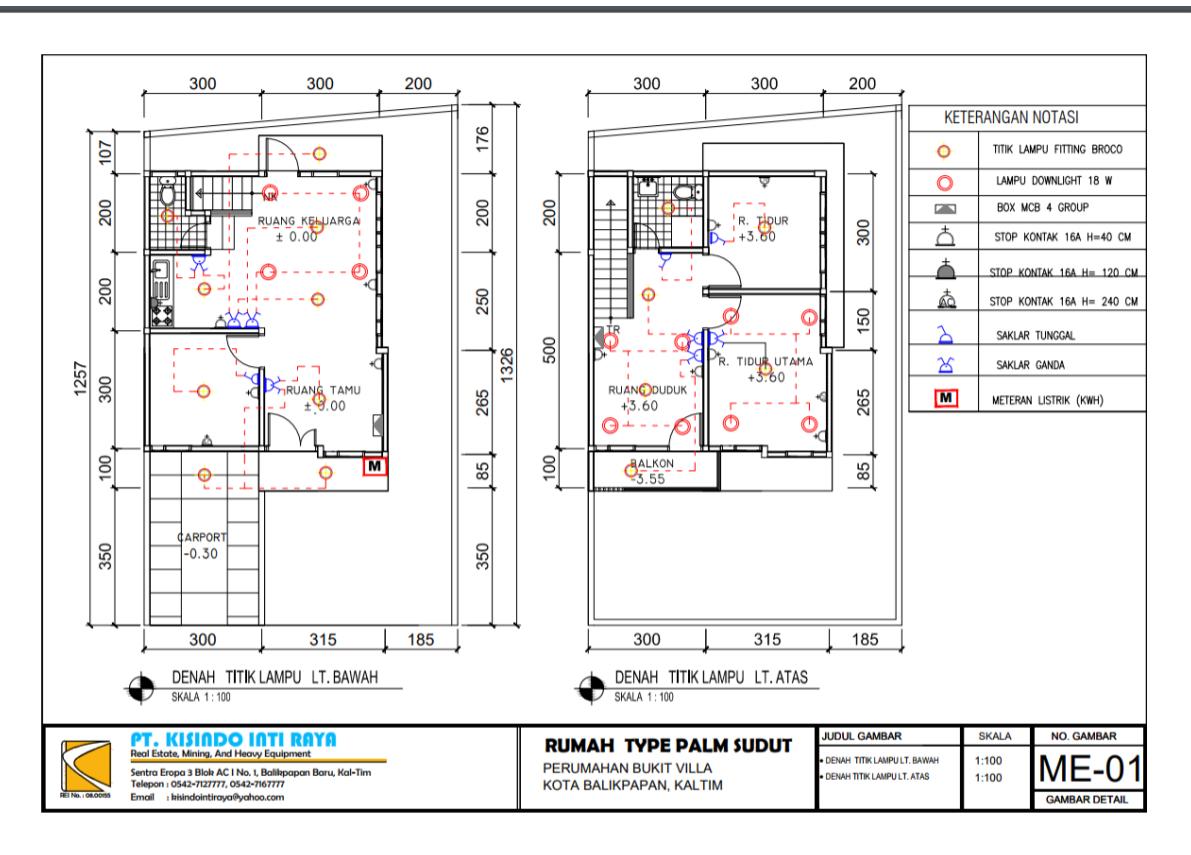

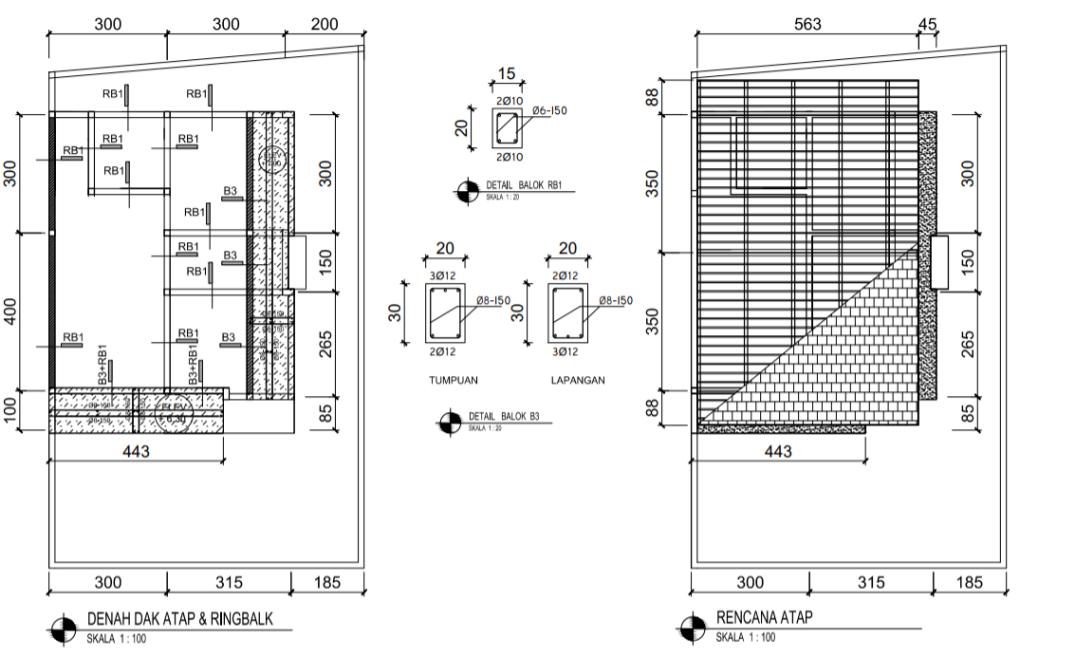

PT. KISINDO INTI RAYA
Real Estate, Mining, And Heavy Equipment
Sentrindo Blok AC I No. 1, Bollipapan Baru, Kalimantan Timur
Telepon : 0542-7127777, 0542-7167777
Email : intiindointiraya@yahoo.com

RUMAH TYPE PALM SUDUT
PERUMAHAN BUKIT VILLA
KOTA BALIKPAPAN, KALTIM

JUDUL GAMBAR	SKALA	NO. GAMBAR
• DENAH DAK ATAP DAN RING BALK	1:100	
• DETAIL BALOK & RINGBALK	1: 20	
• RENCANA ATAP	1:100	GAMBAR DETAIL